




	Tarkett safe.t Granit Dark Sand 0...	466.73 m²		Tarkett vinyl iQ Natural-pink clay, P...	81.16 m²		vloercoating op CD vloer, Coating	185.14 m²
	Desso desert AC89 9523, Tapijtte...	375.74 m²		43.20.02 Coral Brush 5721-hurrica...	45.64 m²		directie levering, M4, PVC Banen / ...	67.02 m²
	Tarkett vinyl iQ Natural-dark war...	685.47 m²		Tarkett vinyl iQ Natural-black, PVC ...	76.18 m²			
	Tarkett vinyl iQ Natural-aqua blue, ...	84.45 m²		PU gietvloer , Ral 7039 met vlok, ...	293.51 m²			
	Tarkett pvc Classics-English Oa...	1004.09 m²		PU gietvloer antislip , Ral 7039 me...	88.74 m²			

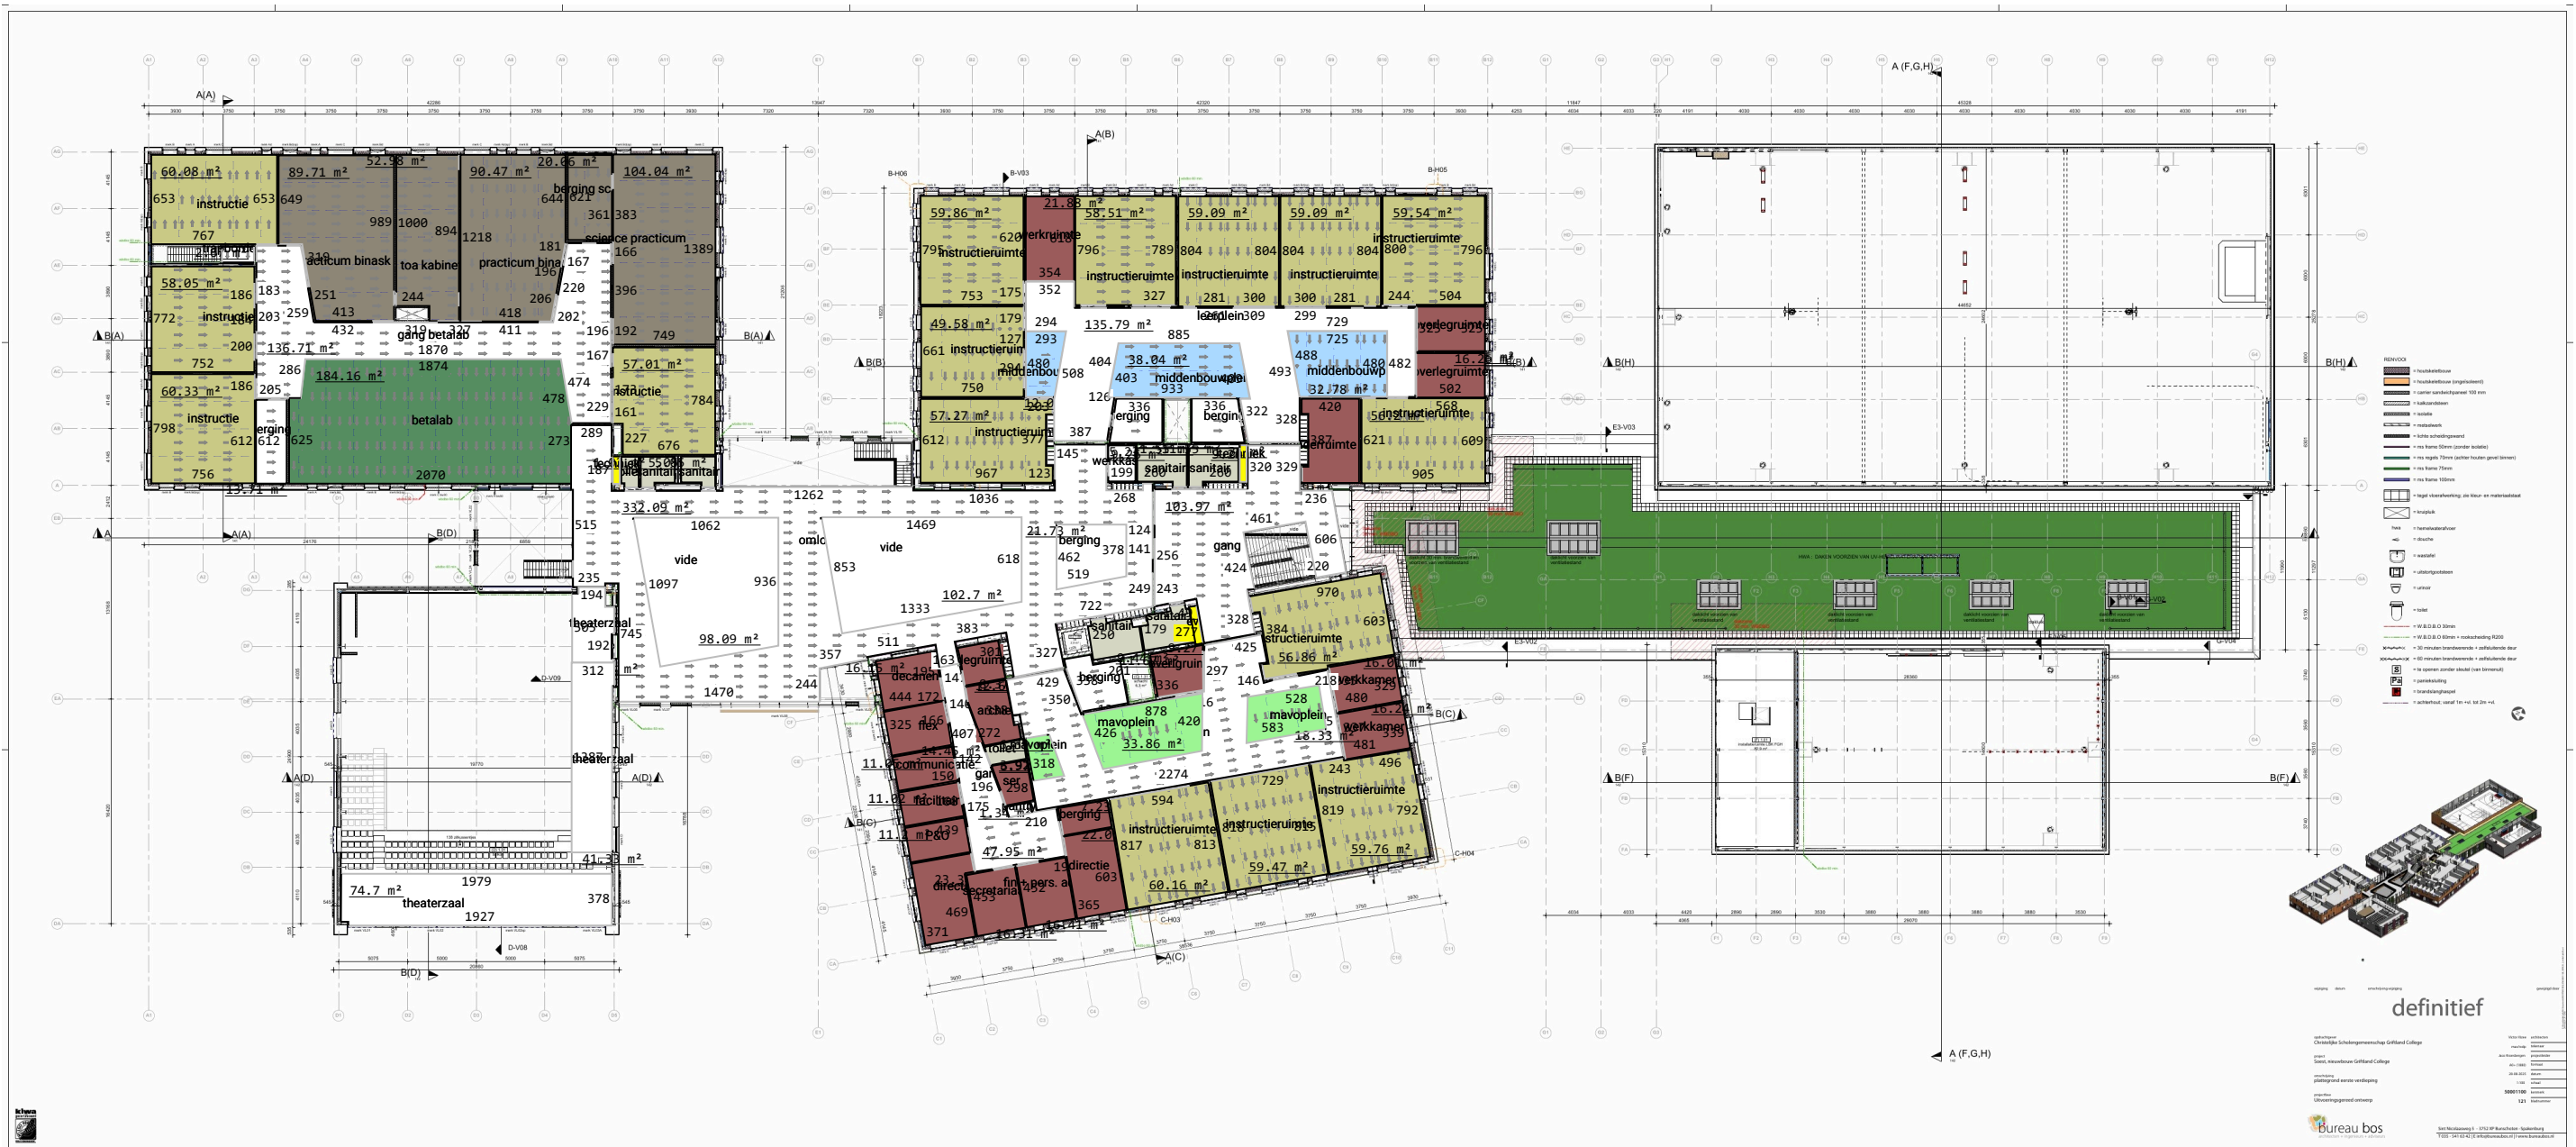



Tarkett safe.t Granit Dark Sand 0508, PVC Banen / Vinyl 357.26 m²

Desso desert AC89 9523, Tapijttegels 299.38 m²

Tarkett vinyl iQ Natural-dark warm grey, PVC Banen / Vinyl 930.87 m²

Tarkett pvc Classics-English Oak grege 55, PVC - LVT 1085.78 m²

PU gietvloer, Ral 7039 met vlok, Coating 54.01 m²

vloercoating op CD vloer, Coating 3.82 m²

Tarkett safe.t Granit light, PVC Banen / Vinyl 184.16 m²

Tarkett vinyl iQ light green, PVC Banen / Vinyl 58.58 m²

Tarkett vinyl iQ Natural-light blue, PVC Banen / Vinyl 82.90 m²

Opdrachtgever : Nicon vloeren
Referentie : 11P251047 Grifla...
Werknr : 251000077
Tekening : verdieping 1 (3/5)

NICON
VLOEREN



 vloercoating op CD vloer, Coating 220.96 m²

Opdrachtgever : Nicon vloeren Schaal : 1:400
Referentie : 11P251047 Grifla... Datum : 03/09/2026
Werknr : 251000077
Tekening : installatie ruimten...

