



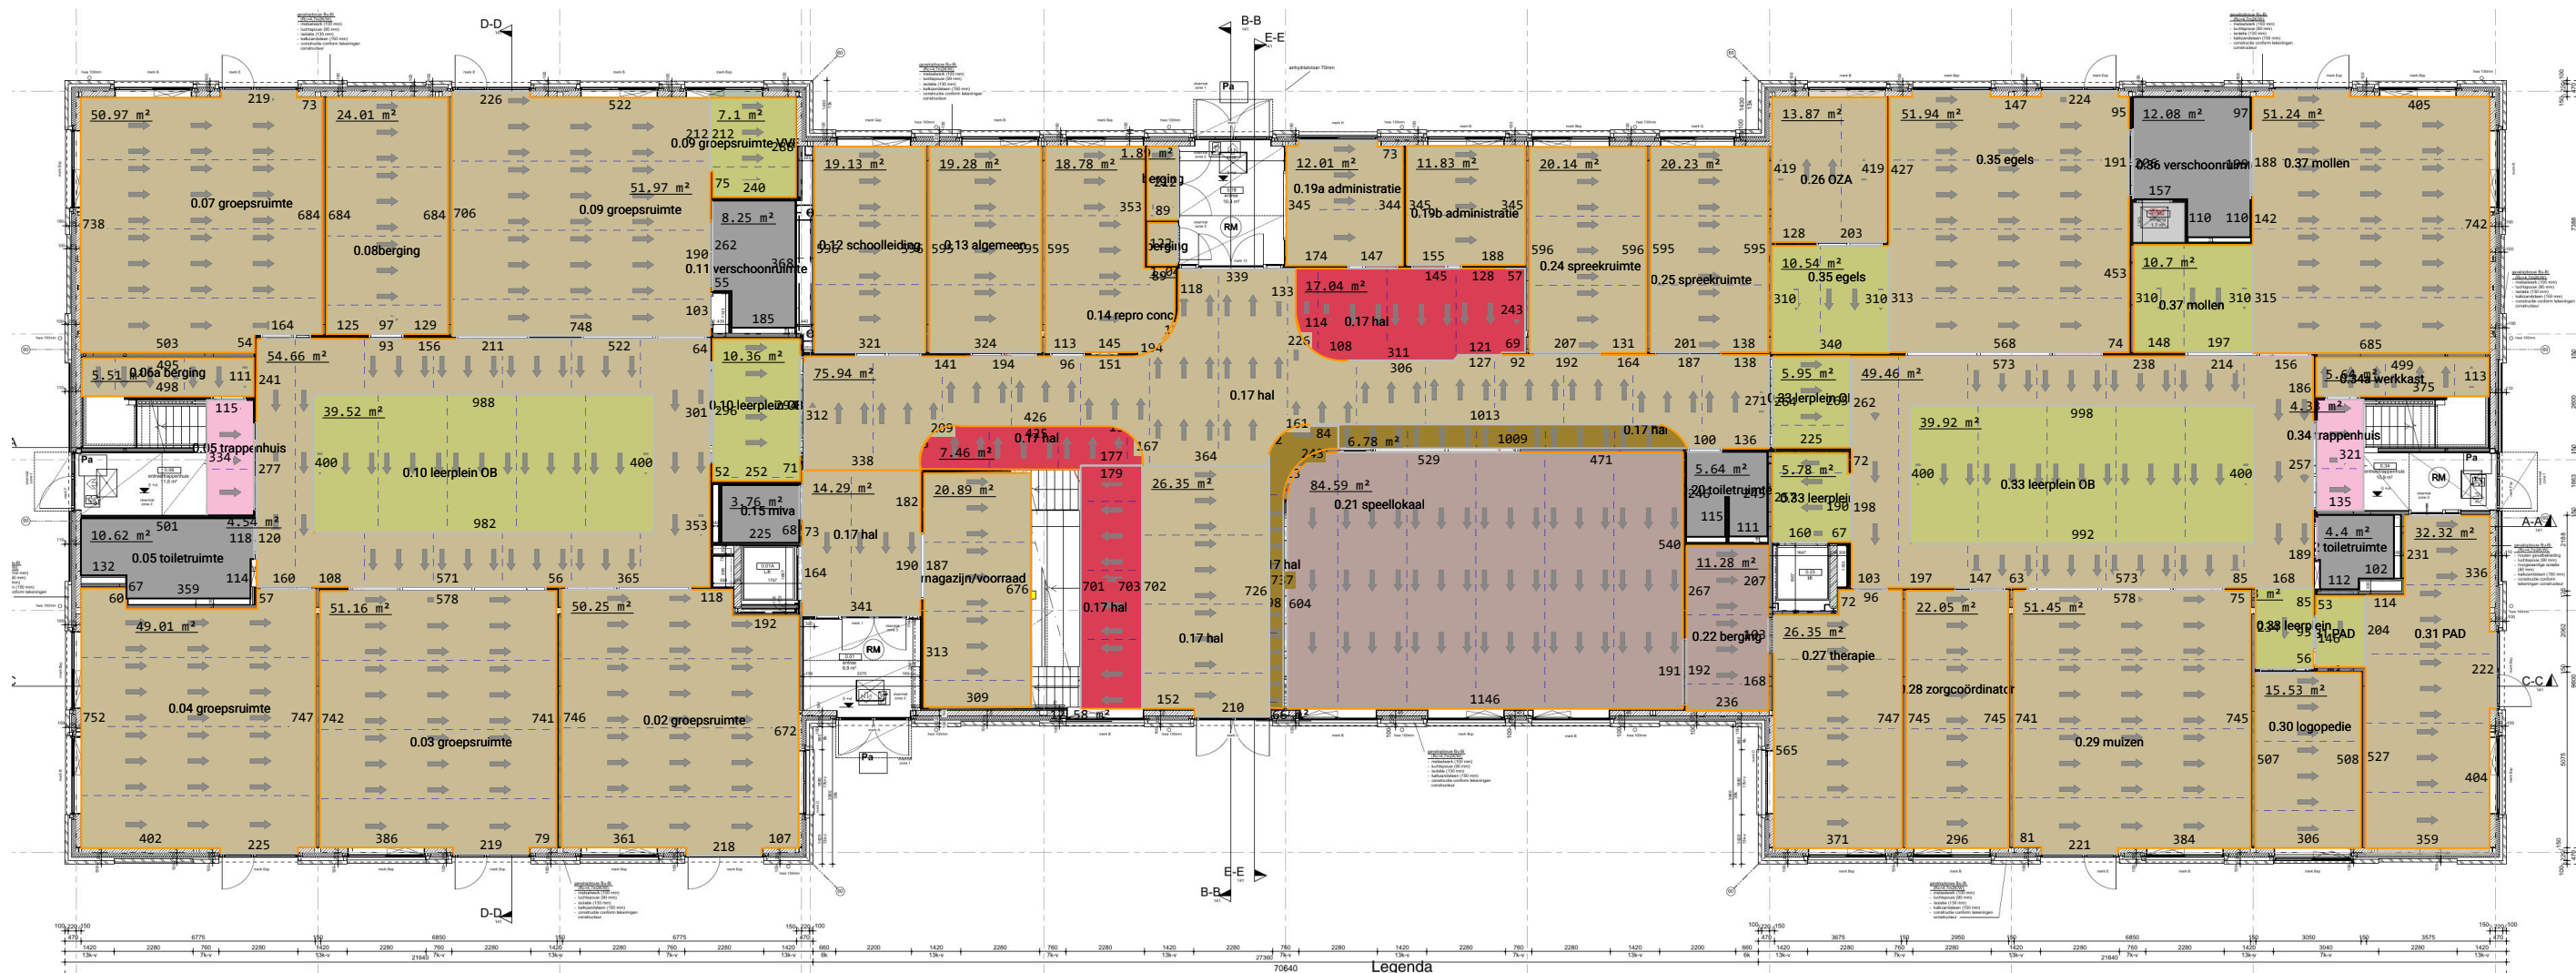

	Marmoleum Real, 3120 rosato, Li...	919.19 m²		Plint, wit, Plinten 50.02 cm			PU gietvloer kleur n.t.b., Coating 44.75 m²	
	Plint, wit, Plinten 494.80 cm			Marmoleum Walton, 3352 berlin re...	37.09 m²		Coral Welcome, 3202 desperado, En...	8.88 m²
	Marmoleum Sport 83020 move, Li...	95.87 m²		Plint, wit, Plinten 15.80 cm				
	Plint, wit, Plinten 35.24 cm			Marmoleum Walton, 3370 terracot...	11.44 m²			
	Marmoleum Walton, 3355 rose...	136.72 m²		Plint, wit, Plinten 14.83 cm				

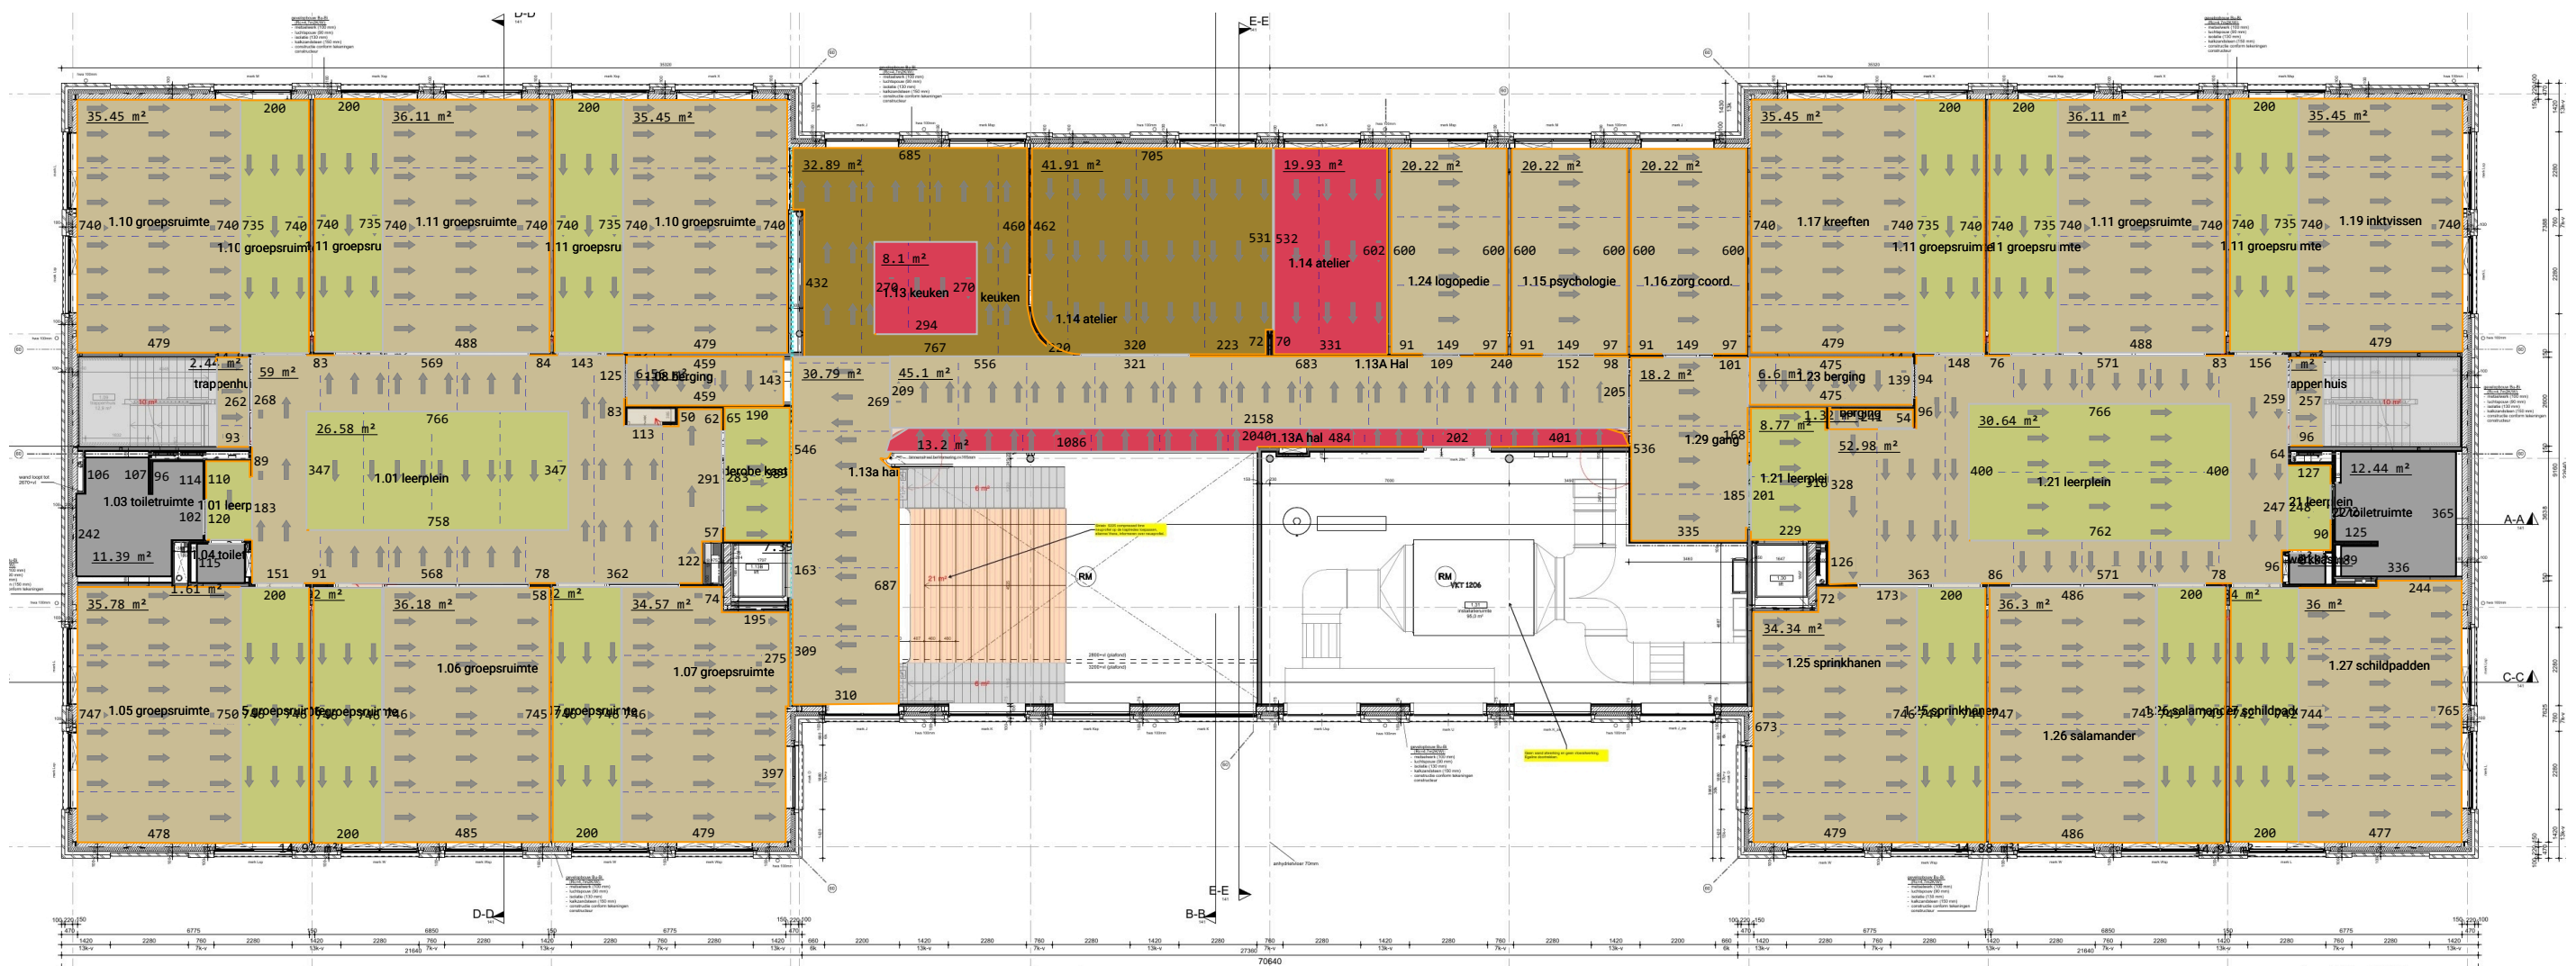

 Marmoleum Real, 3120 rosato, Linoleum 713.32 m²

 Plint, wit, Plinten 329.81 cm

 Marmoleum Walton, 3355 rosemary green, Linoleum 257.79 m²

 Plint, wit, Plinten 136.44 cm

 Marmoleum Walton, 3352 berlin red, Linoleum 41.22 m²

 Plint, wit, Plinten 23.18 cm

 Marmoleum Walton, 3370 terracotta, Linoleum 74.80 m²

 Plint, wit, Plinten 37.23 cm


 PU gietvloer kleur n.t.b., Coating 26.42 m²

Opdrachtgever : Nicon vloeren Schaal : 1:200
 Referentie : 11P260141 Laaks... Datum : 02/09/2026
 Werknr : 260200090
 Tekening : verdieping 1 (3/6)



NICON

 VLOEREN

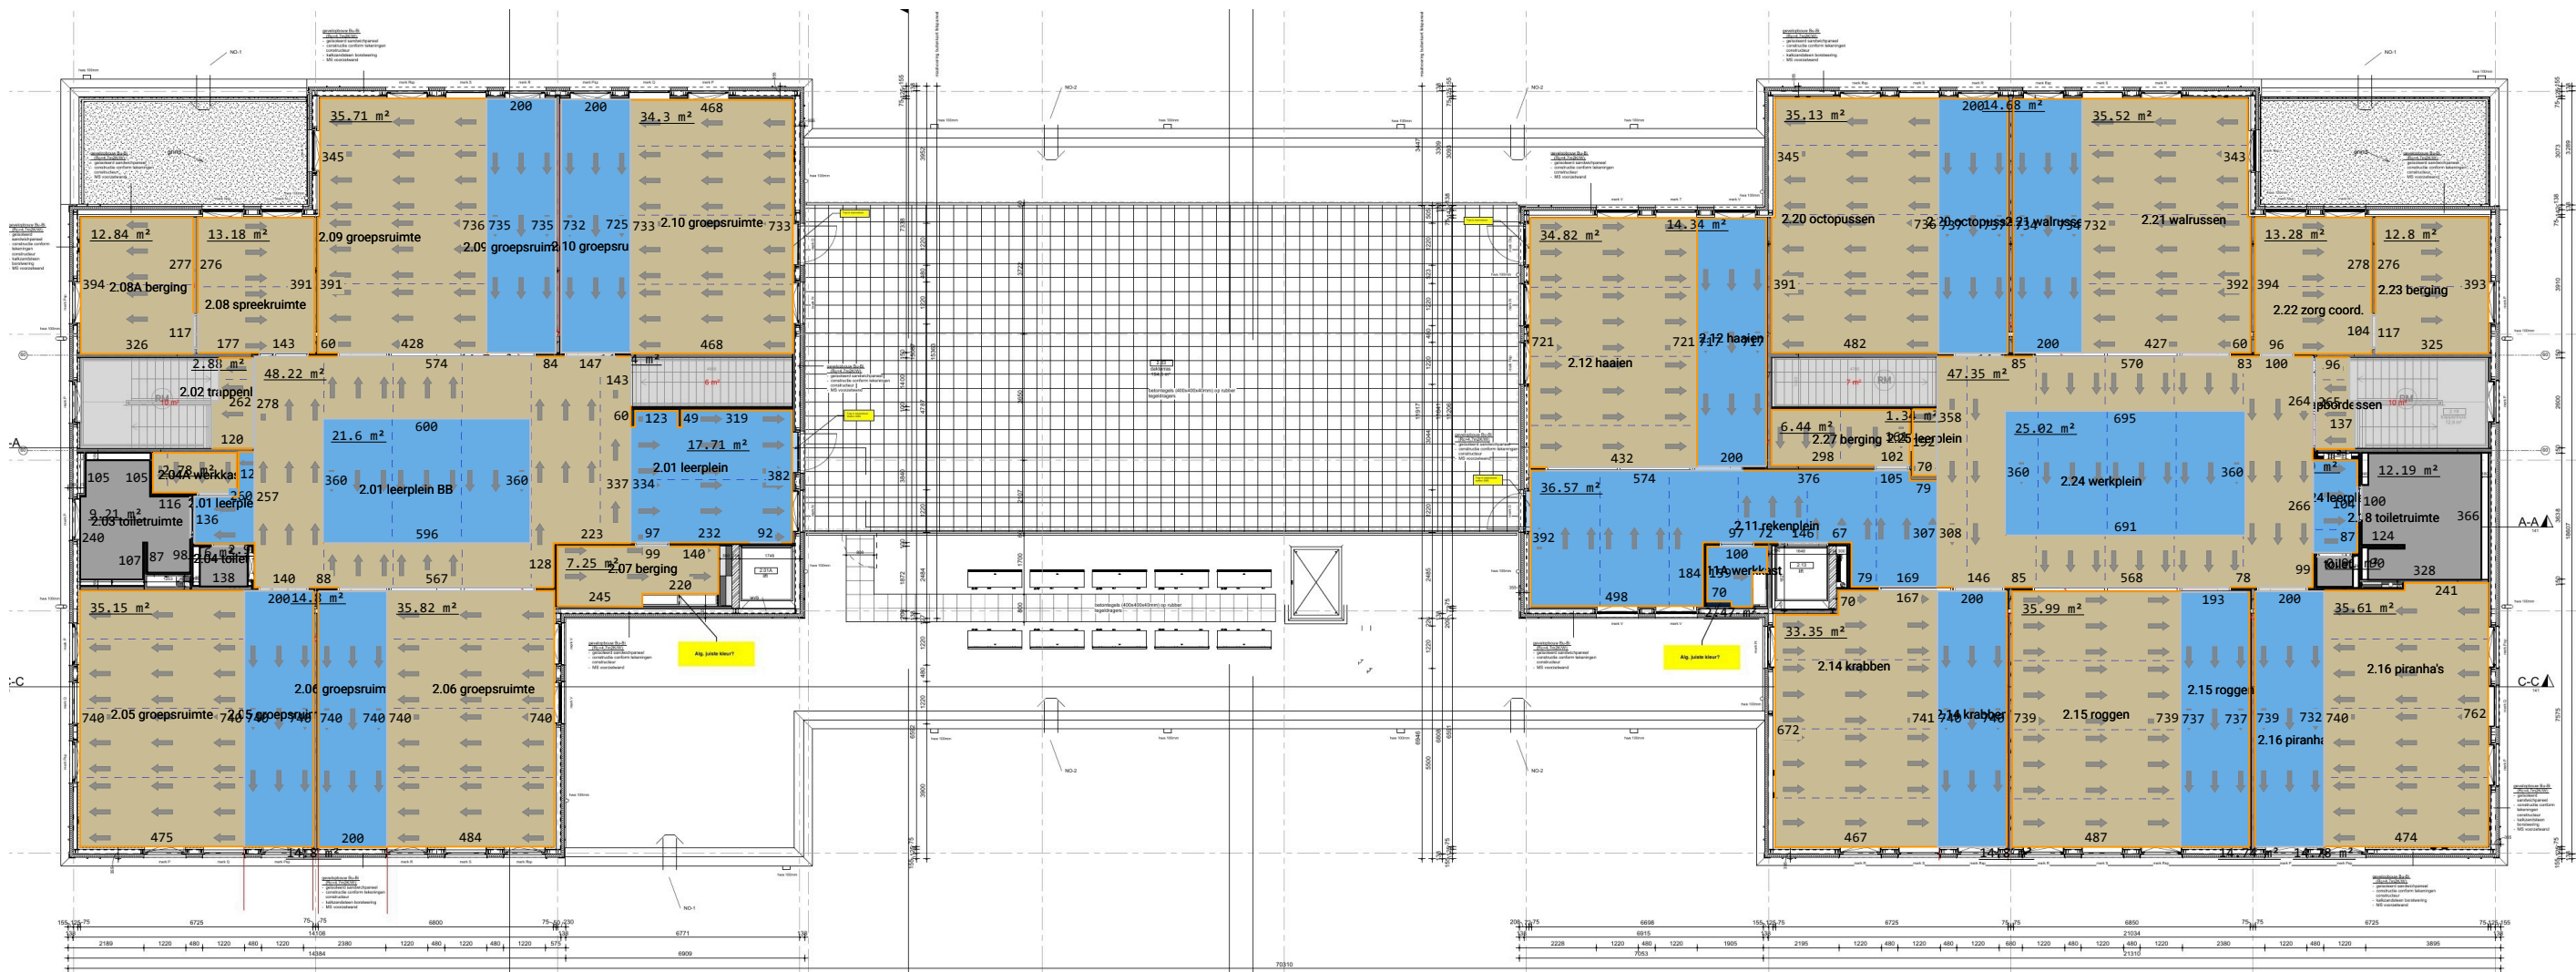

-  Marmoleum Real, 3120 rosato, Linoleum 522.51 m²
-  Plint, wit, Plinten 253.51 cm
-  Marmoleum Walton, 3360 vintage blue, Linoleum 256.74 m²
-  Plint, wit, Plinten 142.52 cm
-  PU gietvloer kleur n.t.b., Coating 23.91 m²

Opdrachtgever : Nicon vloeren

Schaal : 1:200


Referentie : 11P260141 Laaks...

Datum : 02/09/2026

Werknr : 260200090

Tekening : verdieping 2 (4/6)



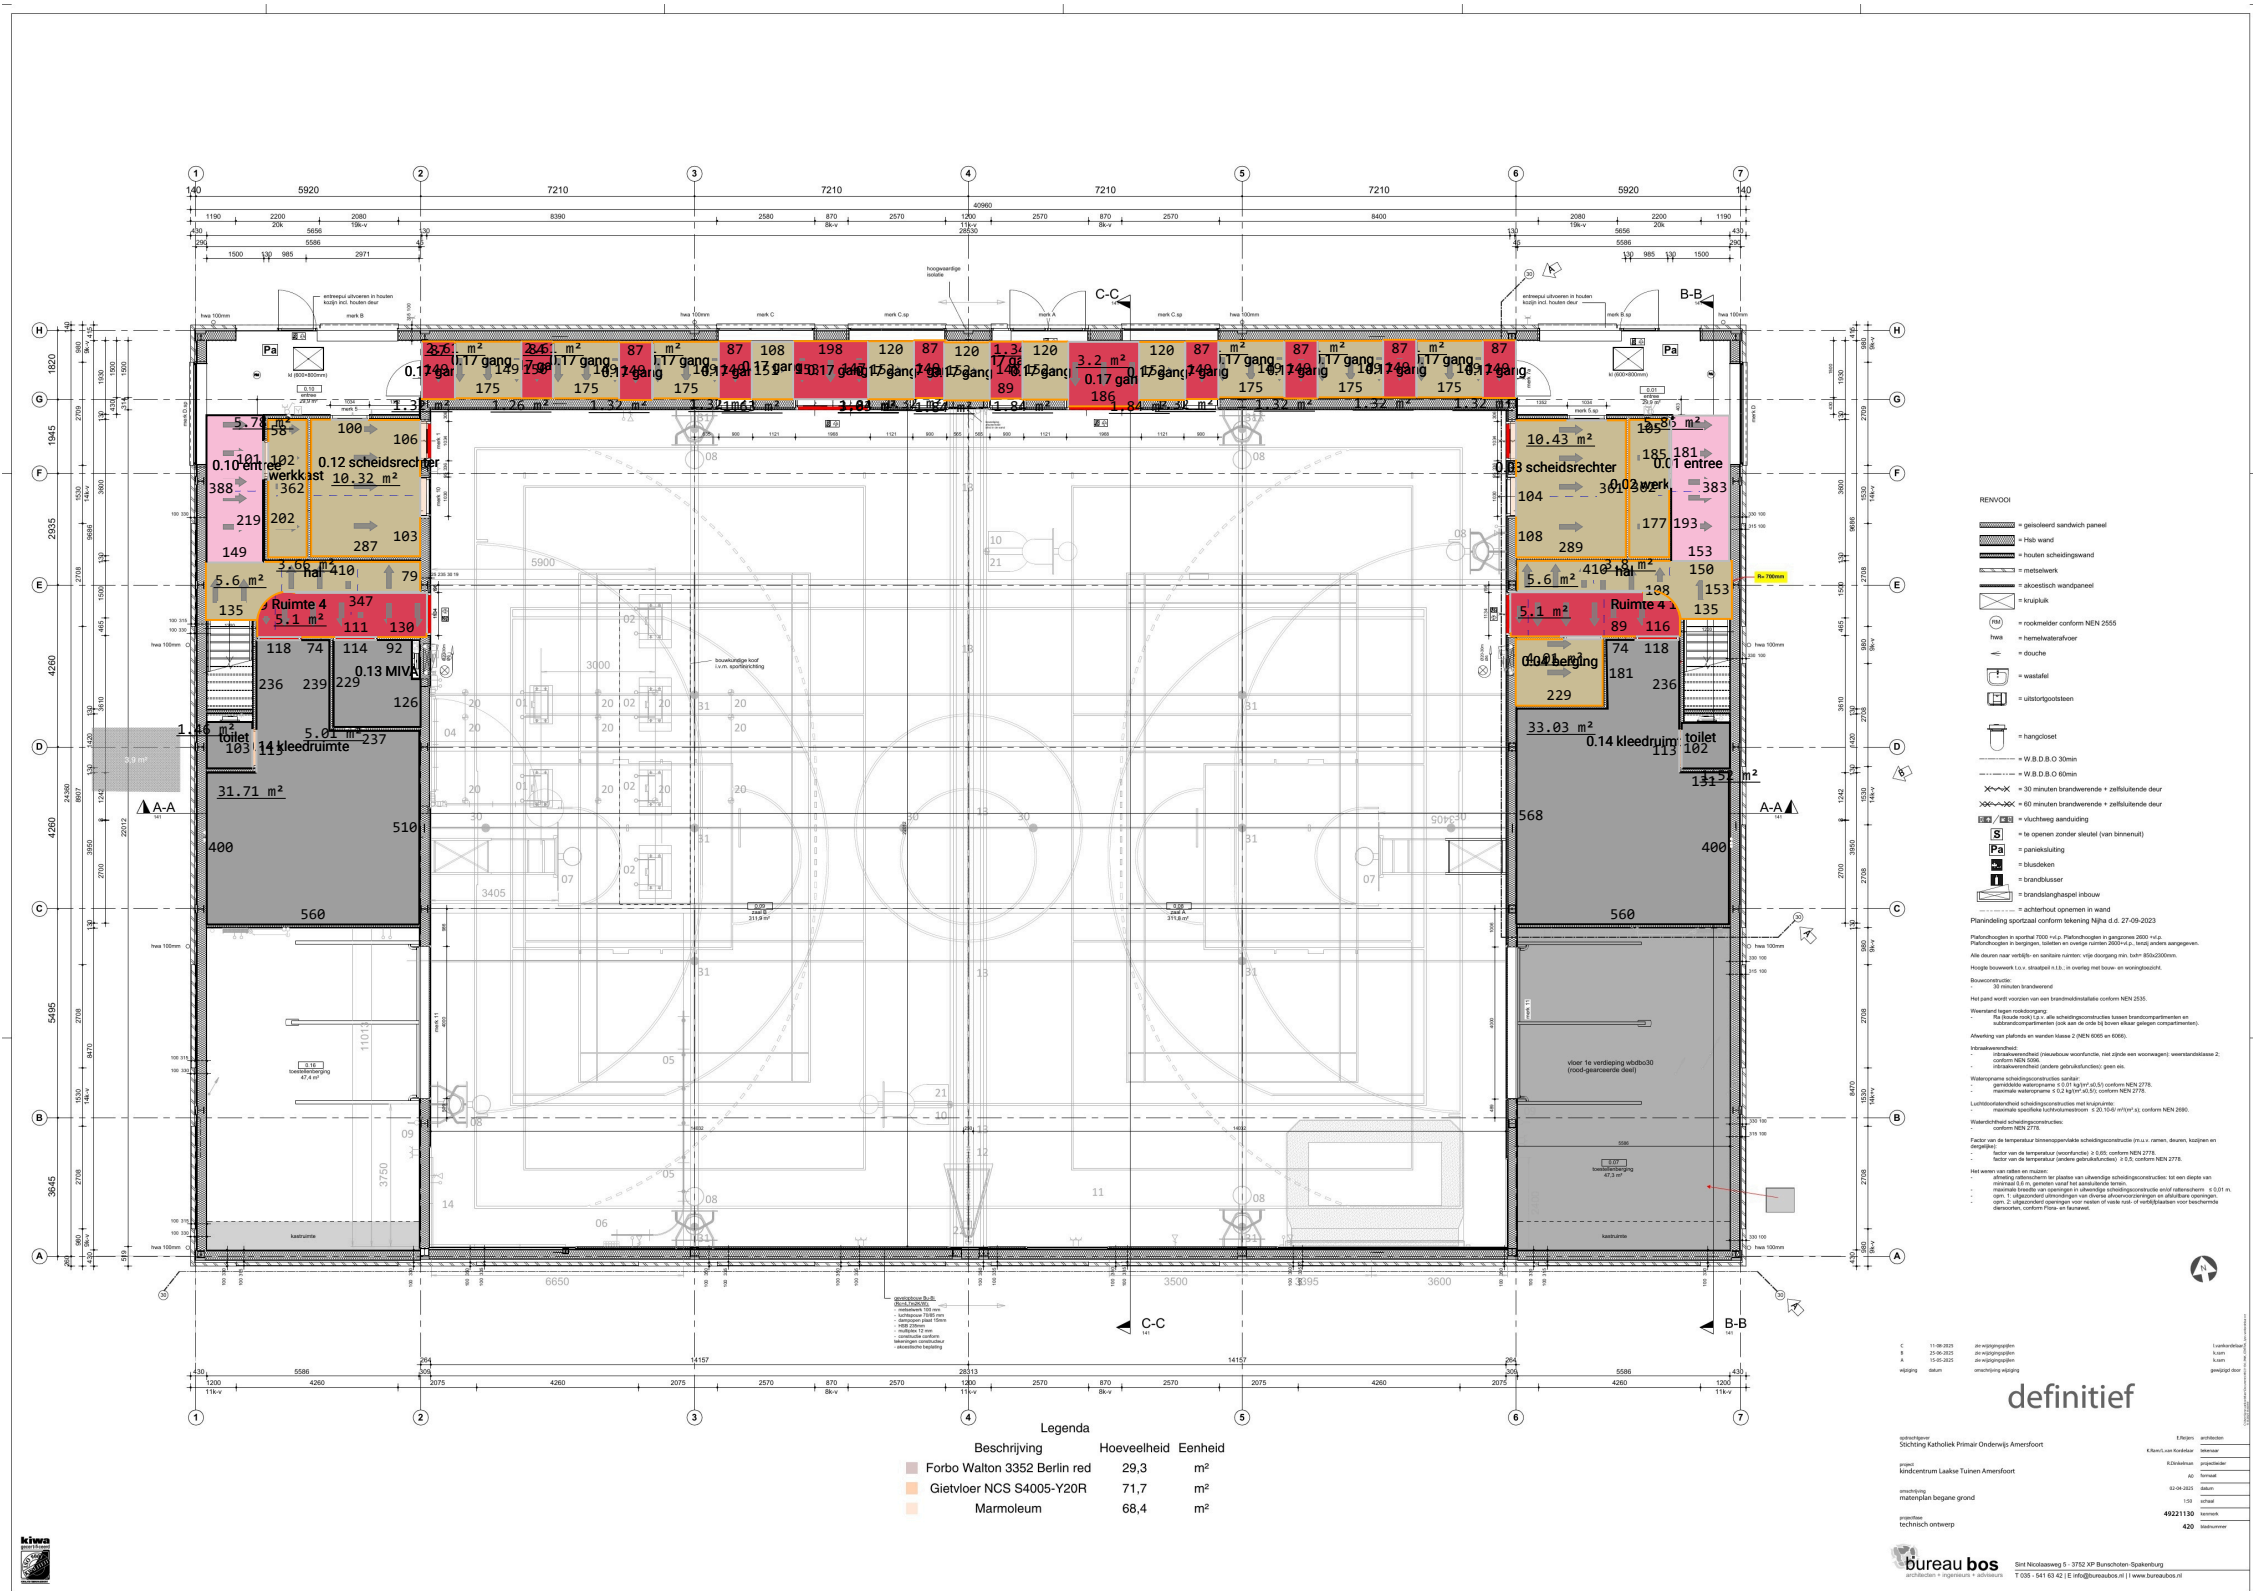

Marmoleum Real, 3120 rosato, Linoleum 68.04 m²

Coral Welcome, 3202 desperado, Entreemat Banen 11.64 m²

Plint, wit, Plinten 93.35 cm

Marmoleum Walton, 3352 berlin red, Linoleum 29.60 m²


Plint, wit, Plinten 29.91 cm

PU gietvloer kleur n.t.b., Coating 72.74 m²

Opdrachtgever : Nicon vloeren
Referentie : 11P260141 Laaks...
Werknr : 260200090
Tekening : begane grond spo...

Schaal : 1:200
Datum : 02/09/2026

NICON
VLOEREN

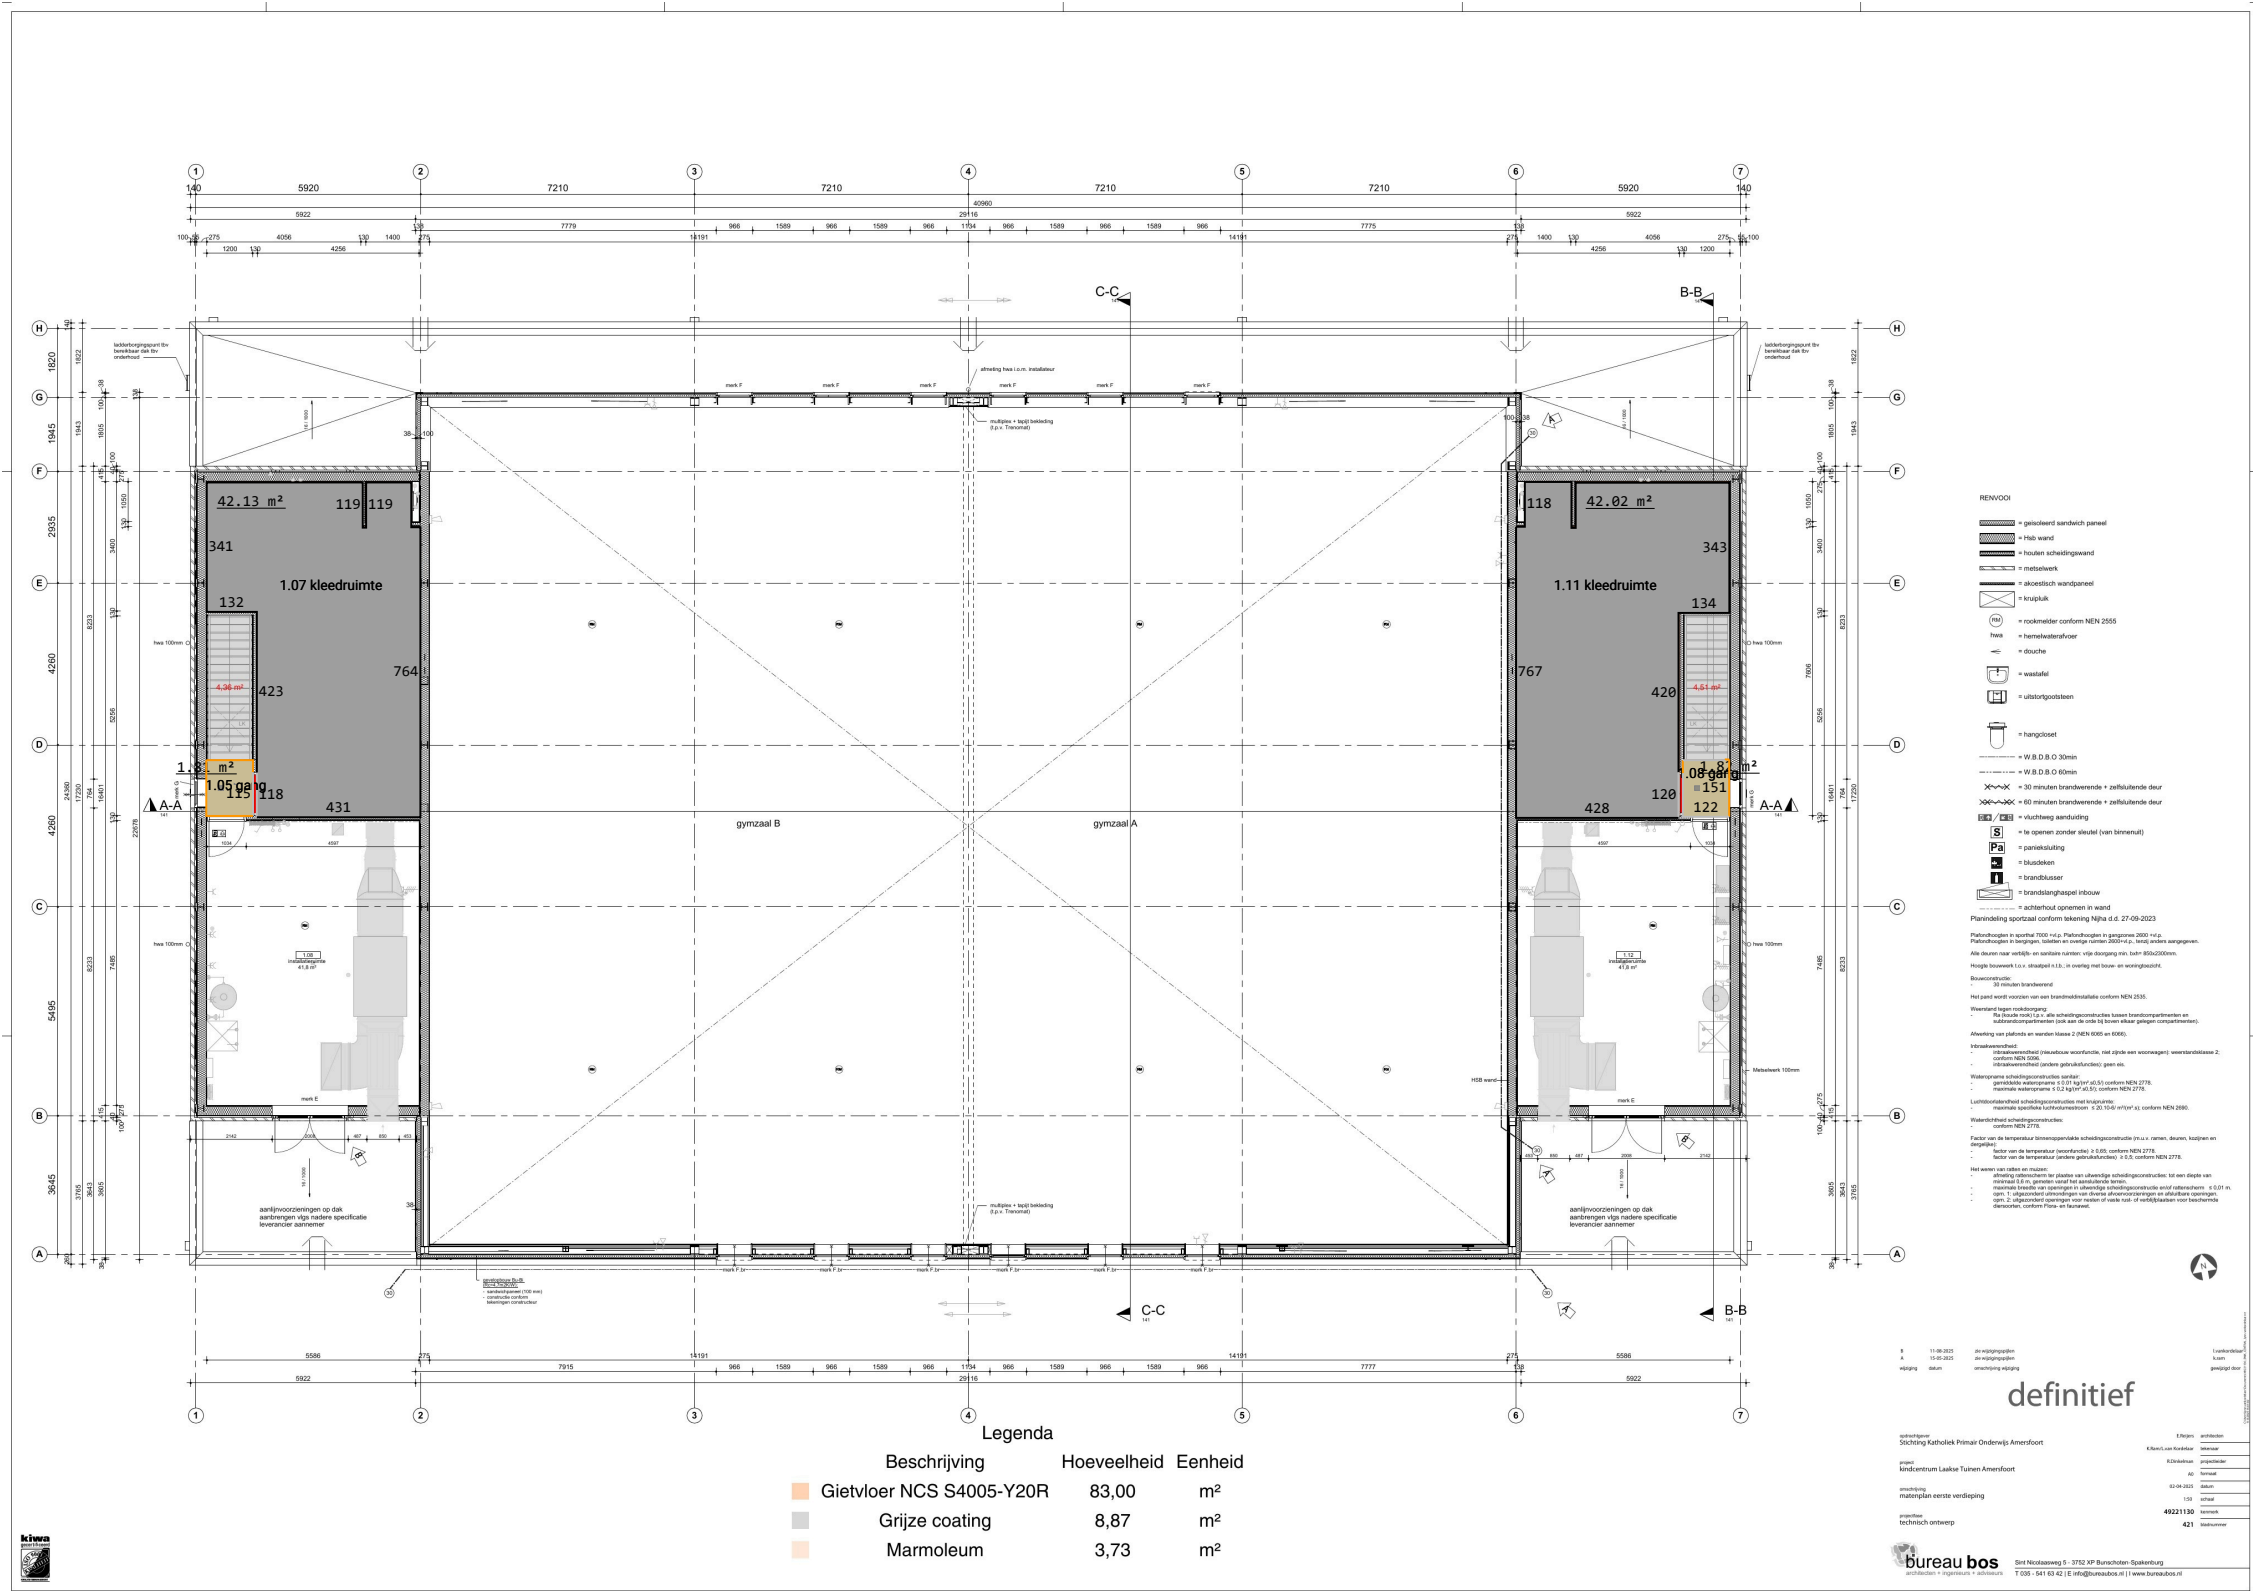

- Marmoleum Real, 3120 rosato, Linoleum 3.63 m²
- Plint, wit, Plinten 6.21 cm
- PU gietvloer kleur n.t.b., Coating 84.14 m²

Opdrachtgever : Nicon vloeren Schaal : 1:200
Referentie : 11P260141 Laaks... Datum : 02/09/2026
Werknr : 260200090
Tekening : verdieping 1 sport...

